






02




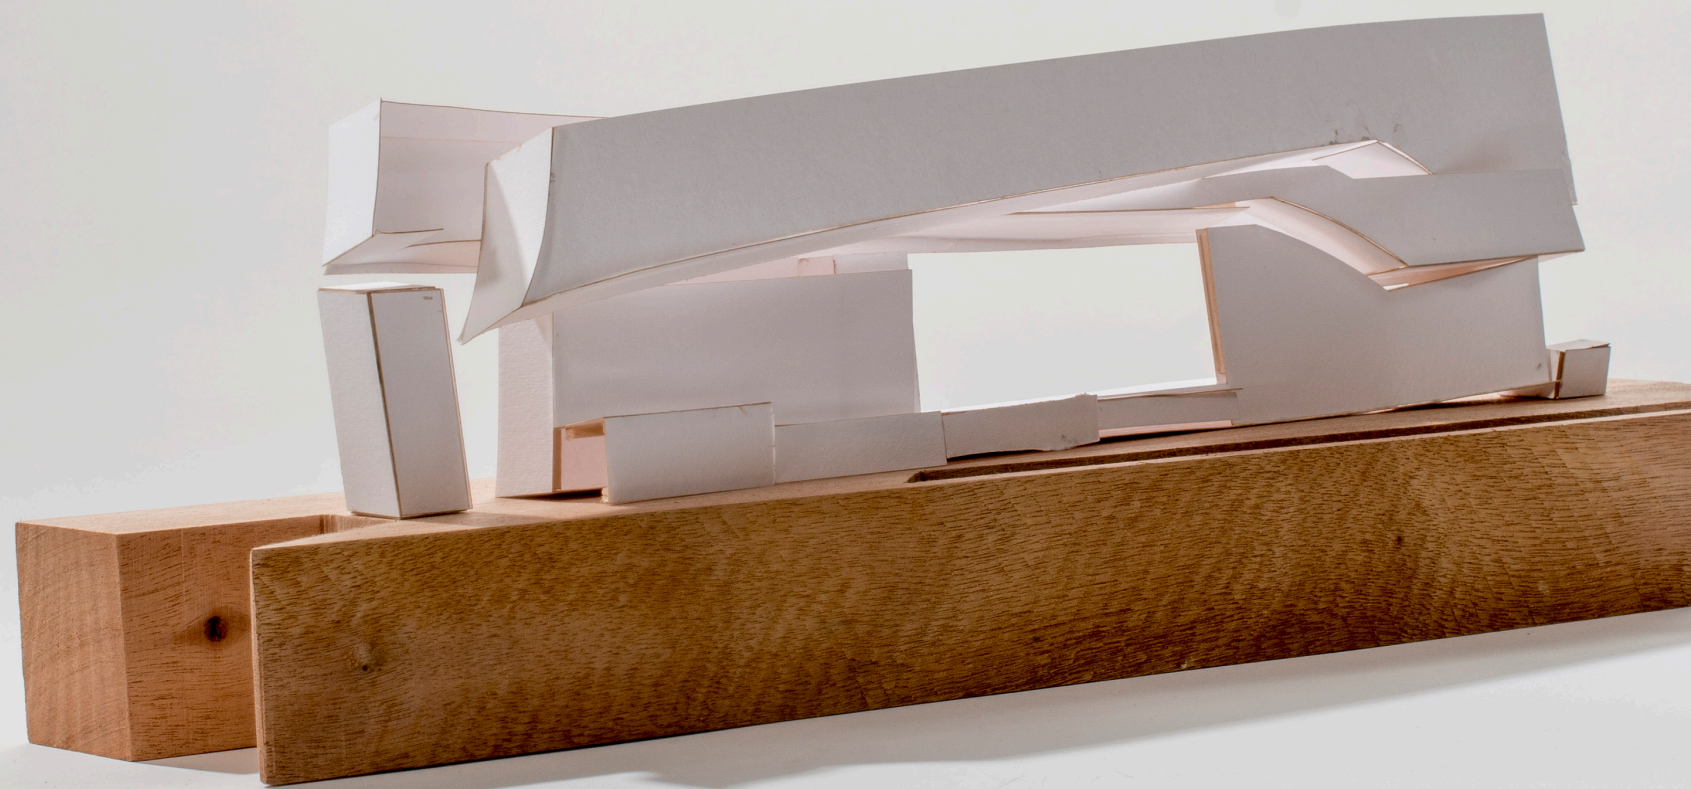


Edges

Form Finding

Location: N/A
Skills: Rhino, Illustrator, Photoshop, Woodworking, Grasshopper

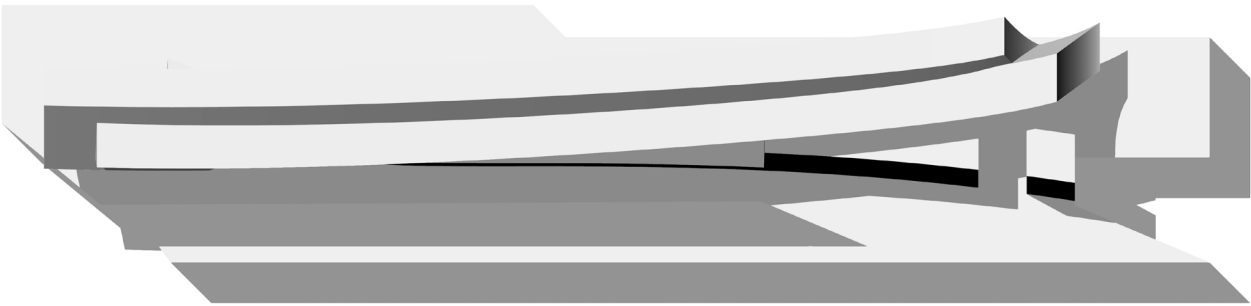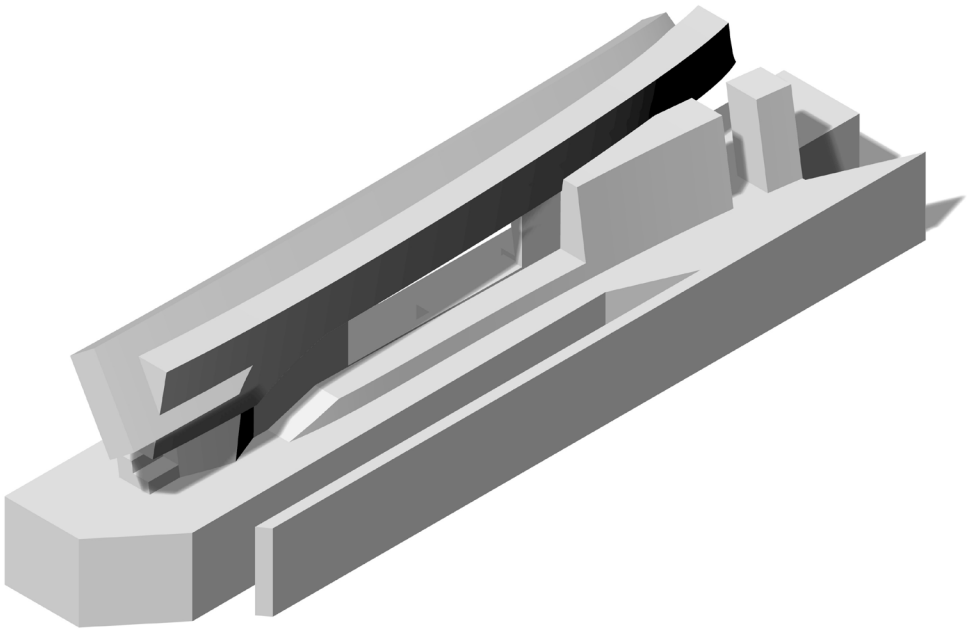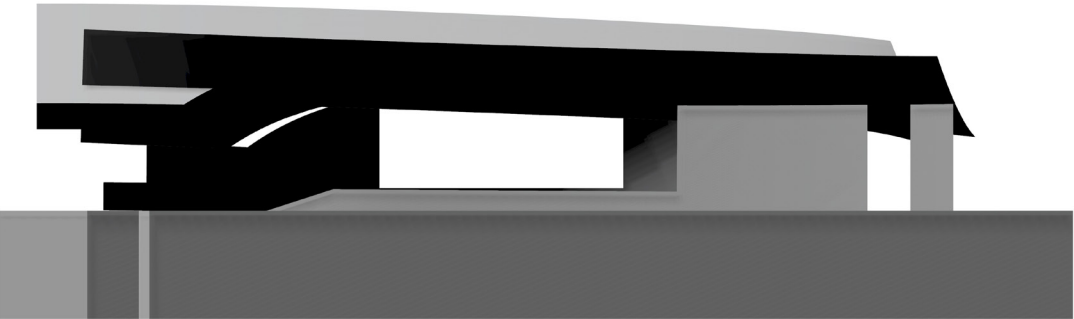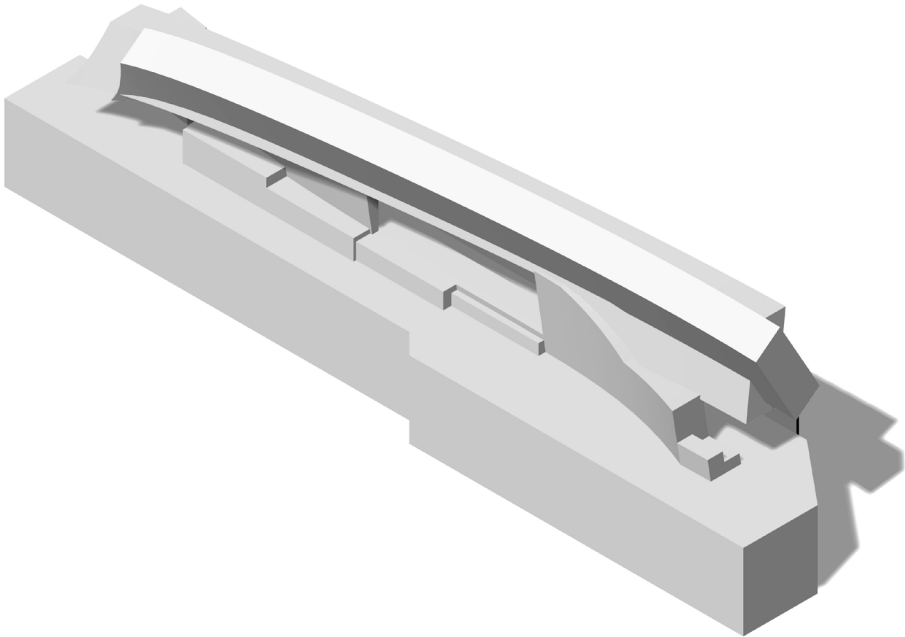

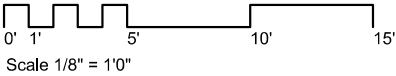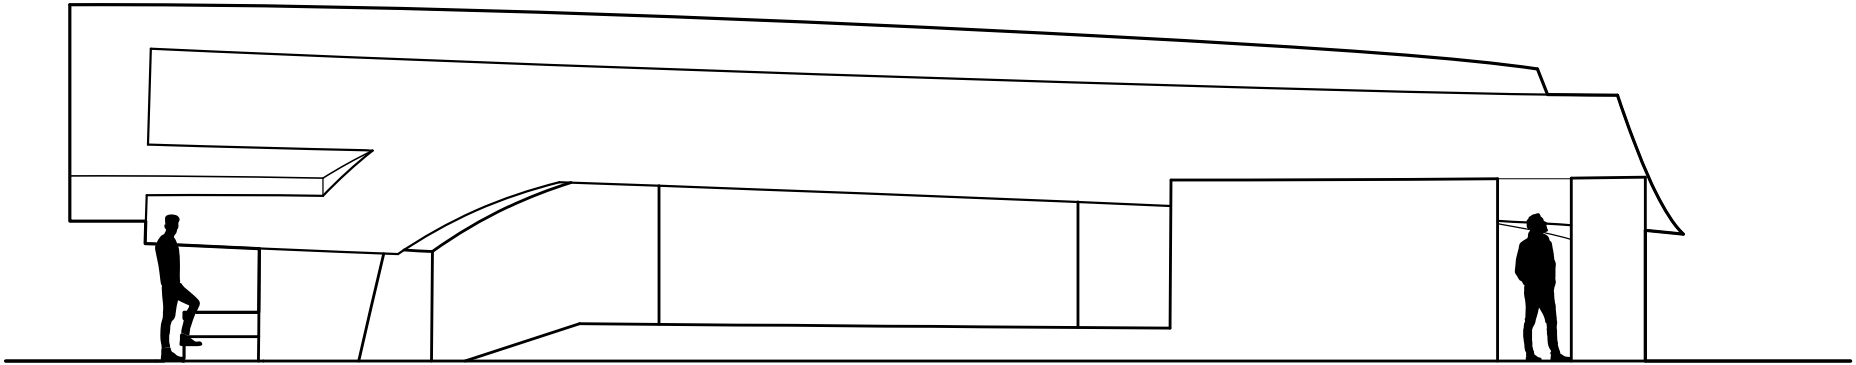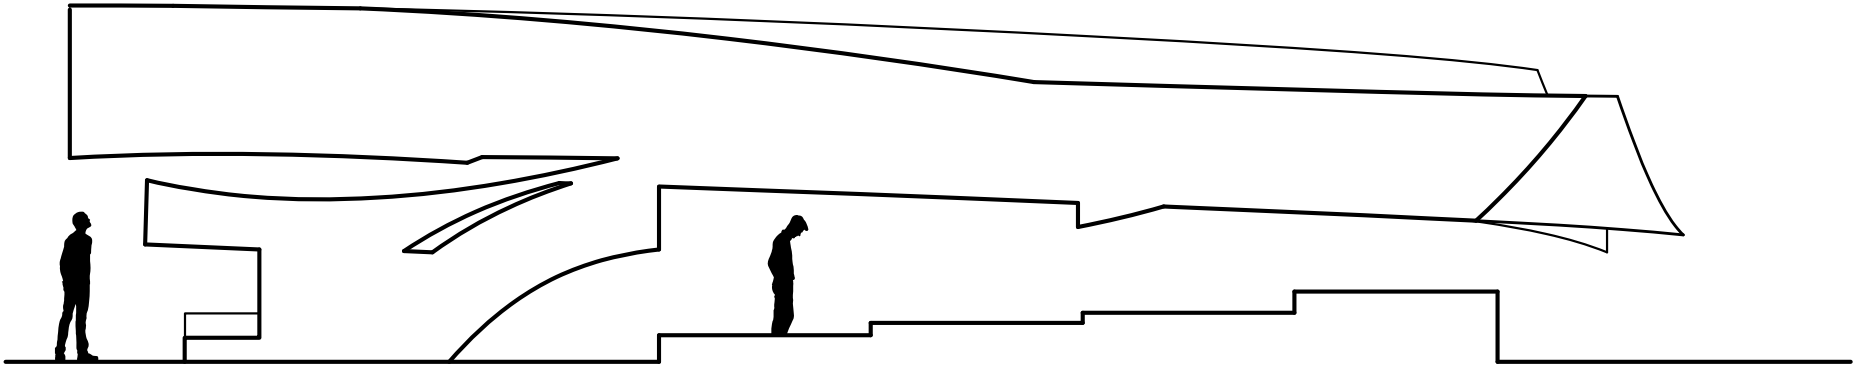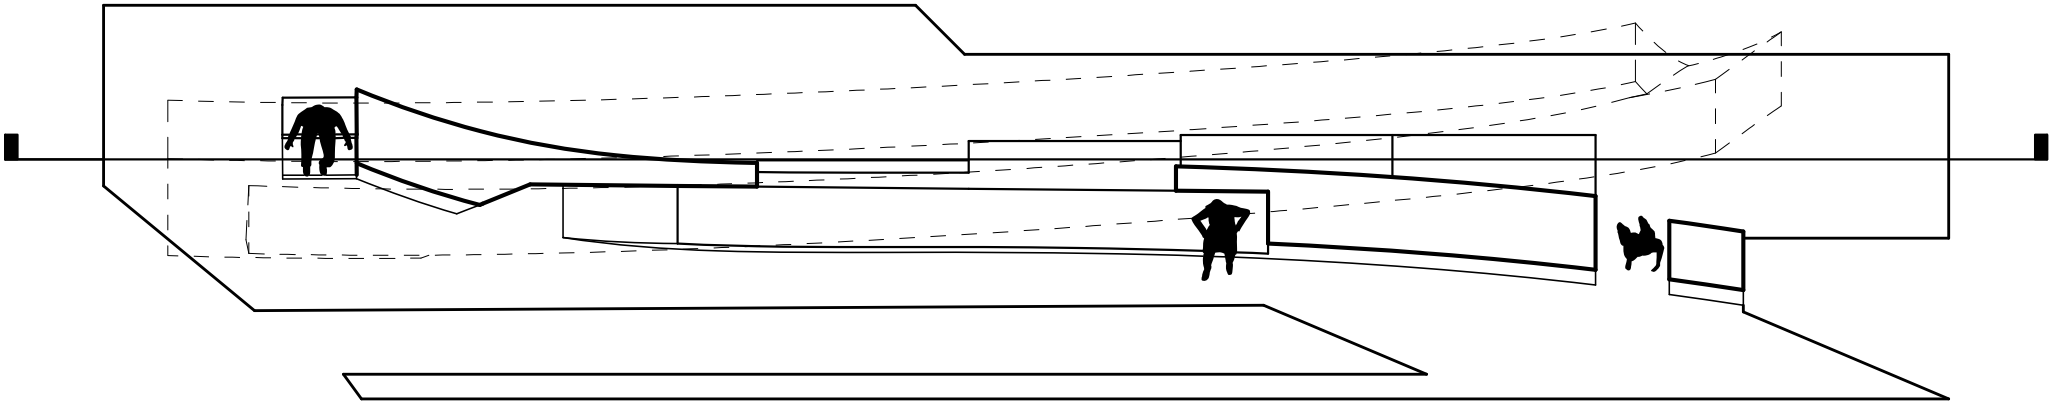



04

Amid the Mist + Steam

Infill California Central Coast Bathhouse

Location: Corner off Nipomo and Higuera St, San Luis Obispo

Software: Rhino, Twinmotion, Illustrator, Photoshop

Project 03: Site Analysis

Introduction

The previous three projects each had a part in the design process of the quarter's final project. Whether that be warming up our site analysis skills in Project 1 at the city scale, creating a formal design language and shaping edges in Project 2, or our specific site analysis at the site scale in Project 3. Project 4 is a proposed bathhouse for the corner of Nipomo and Higuera in downtown San Luis Obispo that aims to bring people together in a space that is neither work or home.

Reflection

Project 4 is closest project so far that I've done to a buildable structure. Everything that's been done in the past 40 weeks of school has led up to this point. This includes developing all the skills necessary to go from concept to final drawings. I was able to combine multiple influences in this model to create something that is unique to city, but also unique in general.

Narrative

An intentional front entry sequence created by a west-oriented ramp leads you through the front entrance as daylighting pierces the main lobby. That is not the only thing that pierces through the main lobby however, which an expanding, jutting circulatory mass creates a sense of curiosity and awe. You're also greeted by both a staircase and the receptionist at the front desk; both pry for your attention. You decide to follow the piercing path and it leads you to a much larger space with another structure overhead showing signs of having more to be discovered. You reach the end of the first path as you hang over multiple feet of ground through a cantilever toward the creek. You go back to the front desk to get your towel and head to the changing room. You're greeted with a small pool as you exit the changing room and bask in its peace. You leave the pool and stay in the lounge before realizing the possible views that could be on the second floor.

The north stars of the project guide circulation from the changing areas to the indoor lobby to the cantilevered sauna on the second floor. The lobby faces the creek forming a connection and a sense of admiration for the site. As a place of gathering and typology that stands out in the U.S., Slow Bath will serve as a new third place for San Luis Obispo in a world that seemingly has little to none left. It will be a place of community, leisure, rest, as well as intellectual and physical embetterment. When it comes to SLO and its community, Slow Bath provides a 24-HR access gender-neutral restroom in addition to its role as a living room for the city. While having an entrance within the bathhouse, it also provides a separate entrance as people lean on the bathhouse when they need it most.

Precedents


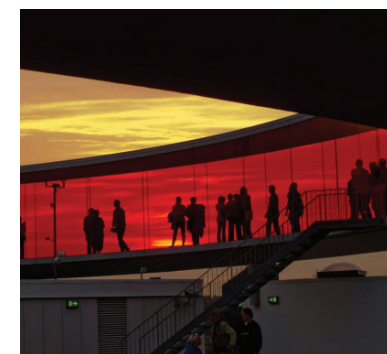






Photo courtesy of olafureliasson.com


Both of these projects have a unique approach when it comes to framing its context. Where "Your Rainbow Panorama" by Studio Olafur Eliasson sees circulation path and viewport as one, the Slow House by Diller Scofidio + Renfro takes an opposite approach. The latter uses an expanding mass as a model for a home where it takes on a skeletal form to frame the view the Hampton ocean view.



Photo courtesy of dsrny.com

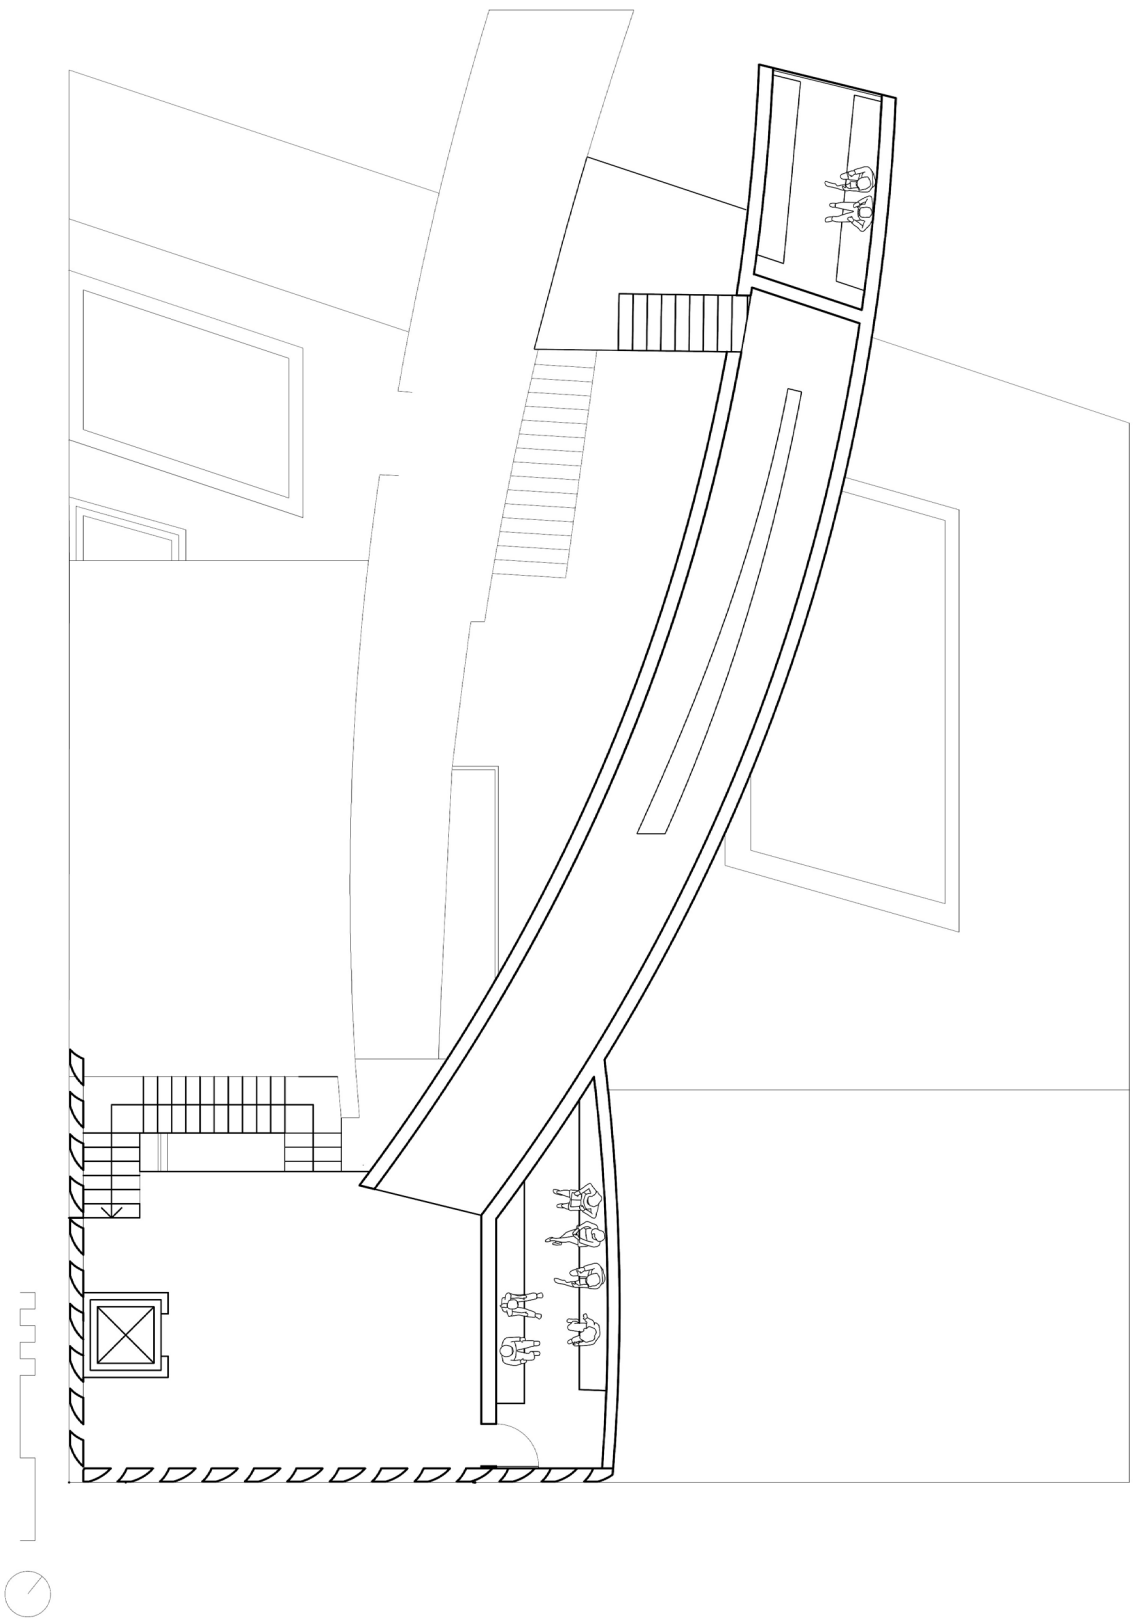

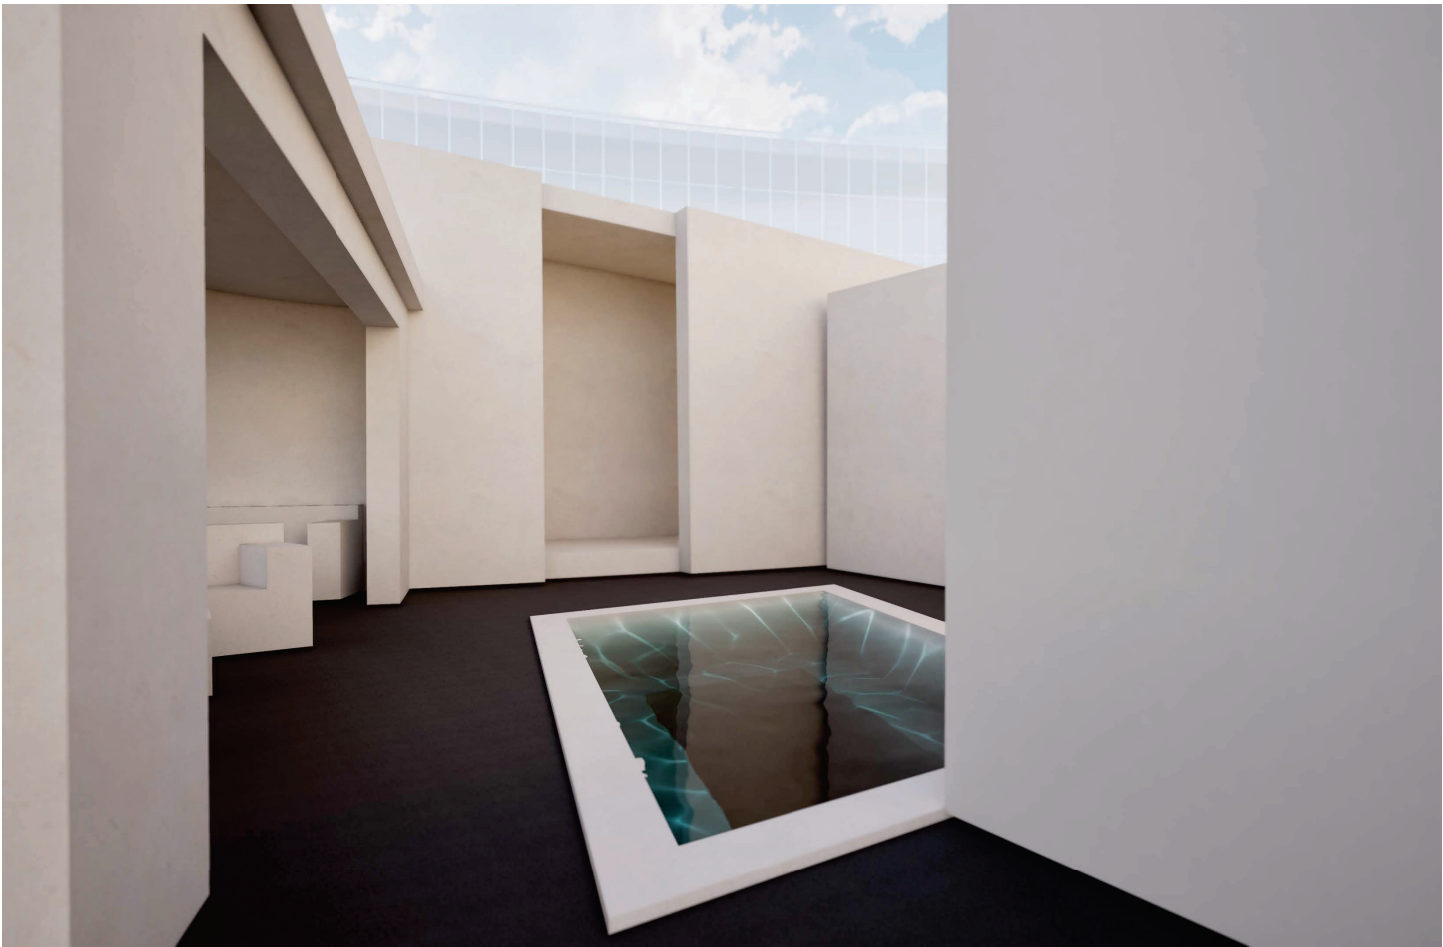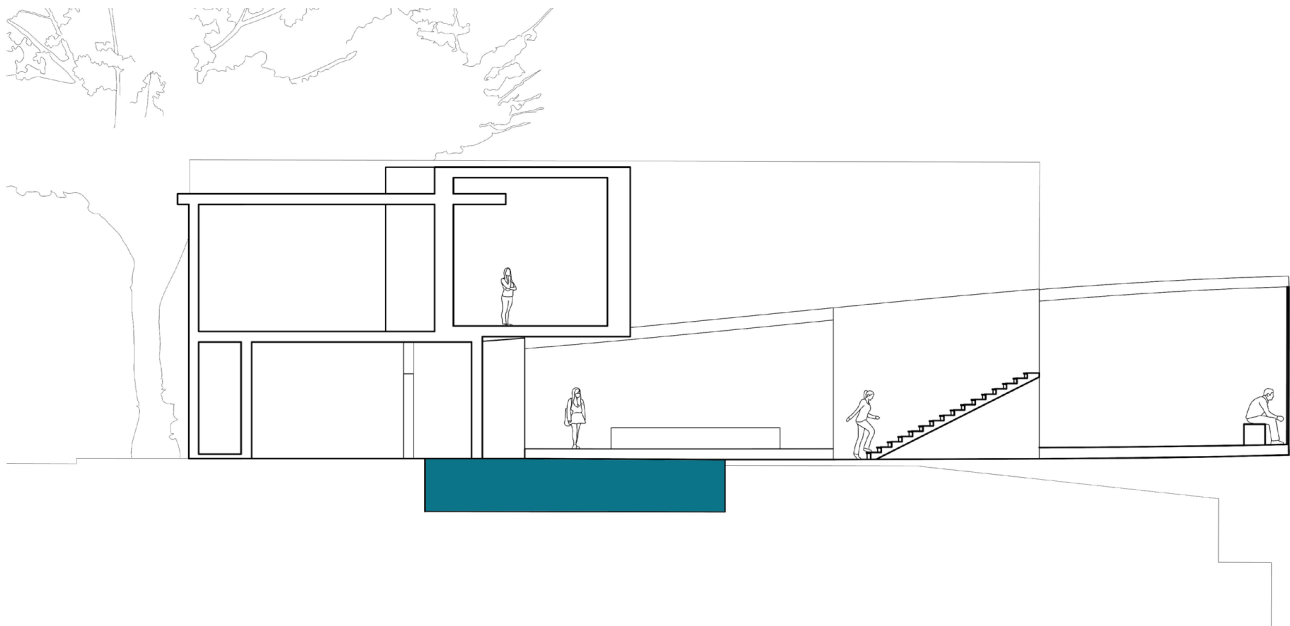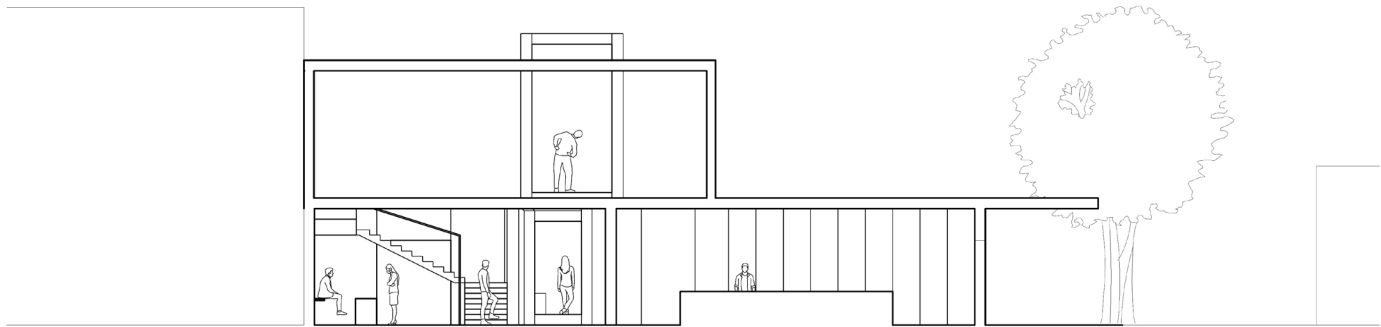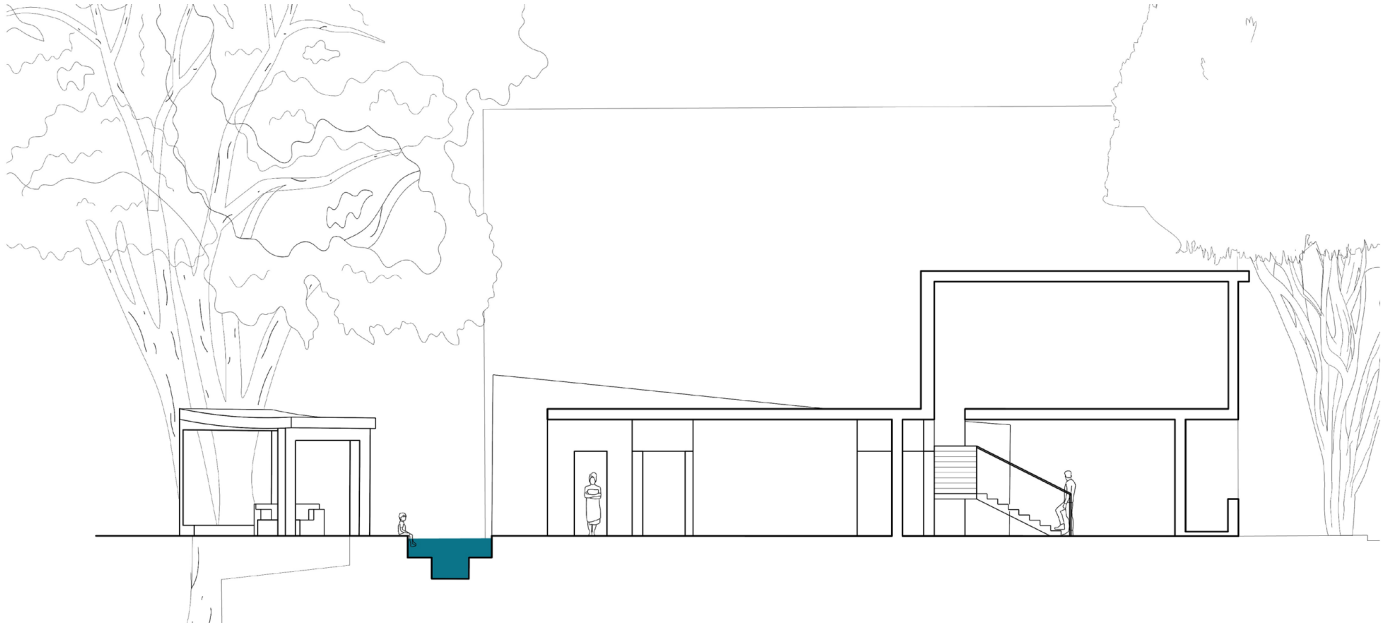

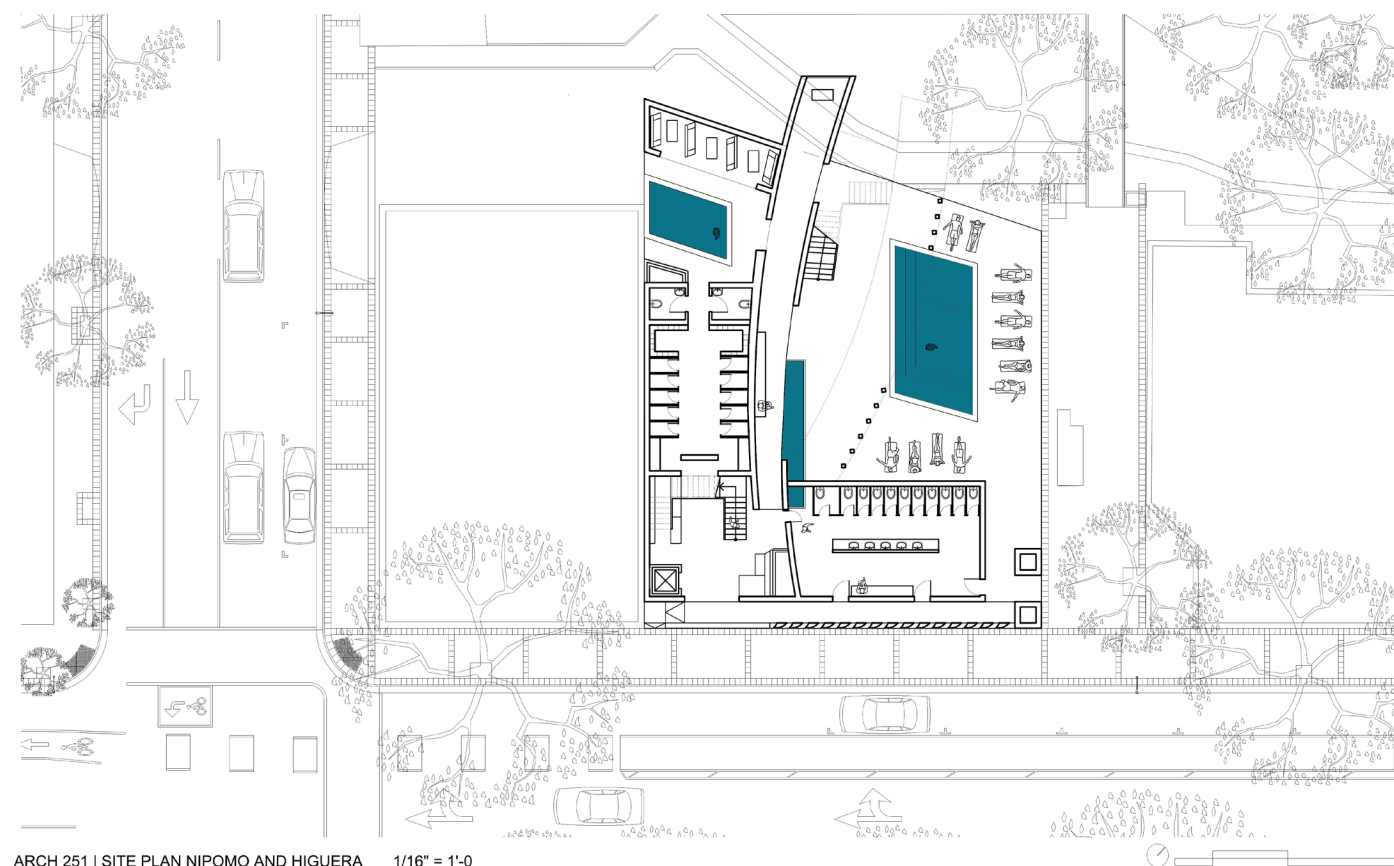


ARCH 251 | SITE PLAN NIPOMO AND HIGUERA 1/16" = 1'-0

Concept Statement



2 masses pierce through the lobby creating a sense of dynamism and intrigue immediately upon entry. One's circulatory experience is intuitive, intentional, and ever changing through the use of the masses. Views of San Luis Obispo and its creek are highlighted and celebrated where viewing portals are created at a dedicated viewing center, indoor lobby, and sauna.

Logics


- 1. Pierce** Masses pierce through spacial edges creating dynamism in form and light conditions. Stemming from the idea of intersecting mass, two beacons of mass pierce through like a pencil to paper.
- 2. Extrude** Stemming from one of the verbs in Project 2, to extrude is to extend a face or a part of a face that sticks out in comparison to its surroundings. This logic largely dictates how space is created and curated throughout the project.
- 3. Carve** As important is the mass, the void, and subsequently space, is created through carving. This stems from another project 2 verb, which aids in achieving the goal of purposeful and habitable daylighting conditions.

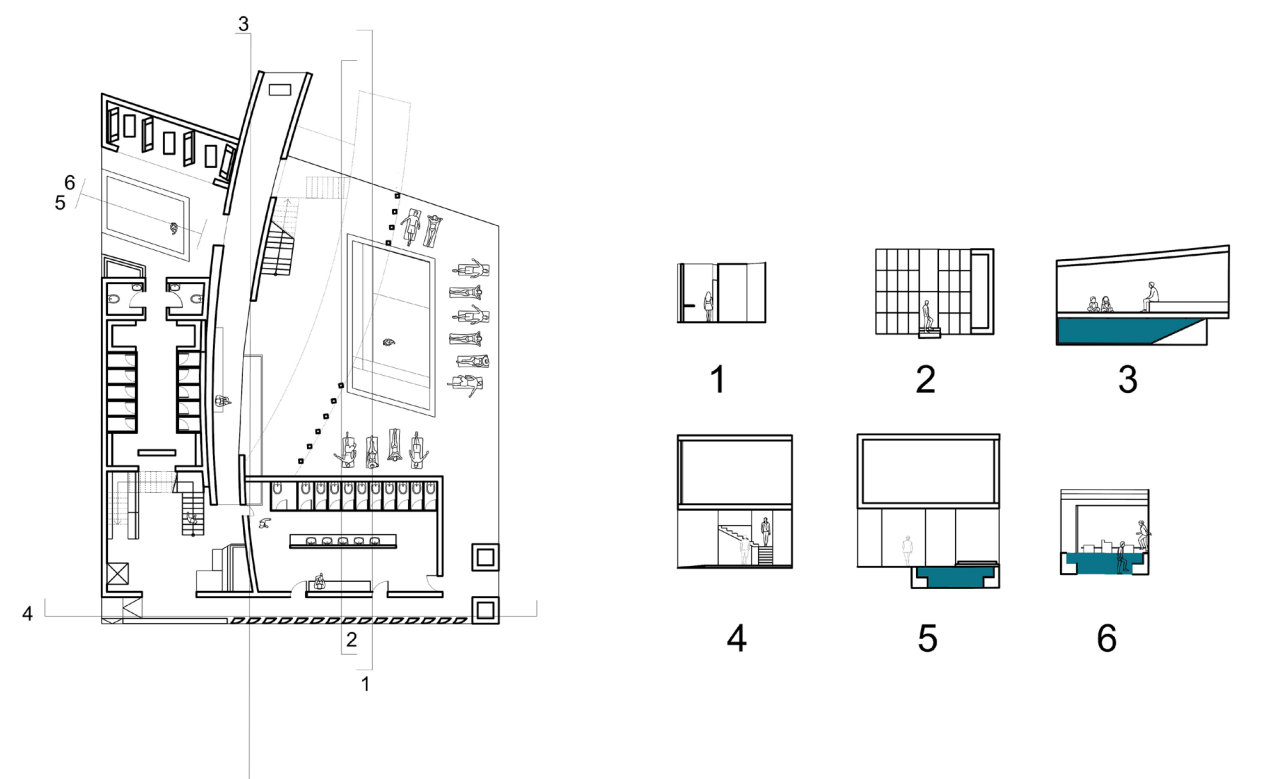


Concept Diagram

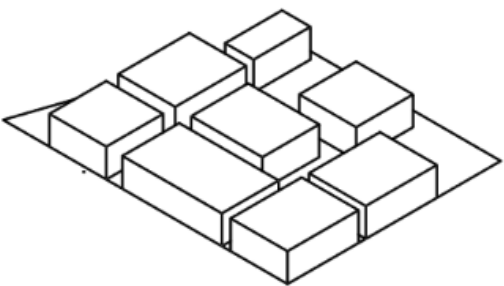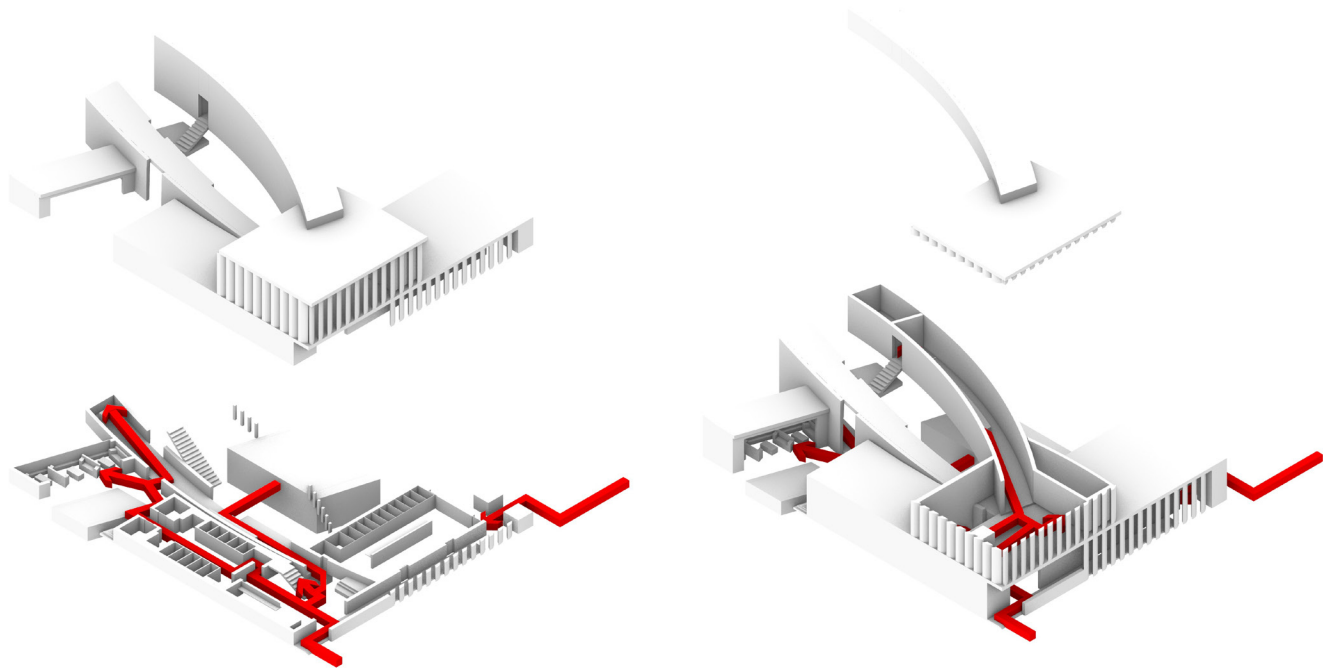


1. Massing of Required Square Footage for Each Space

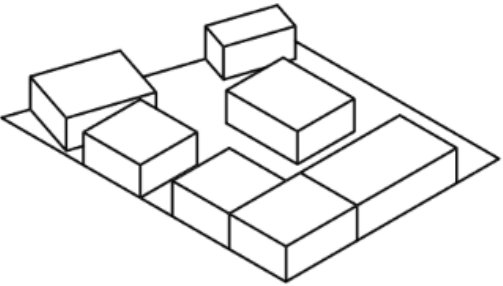


2. Arrange to Optimize for Circulation

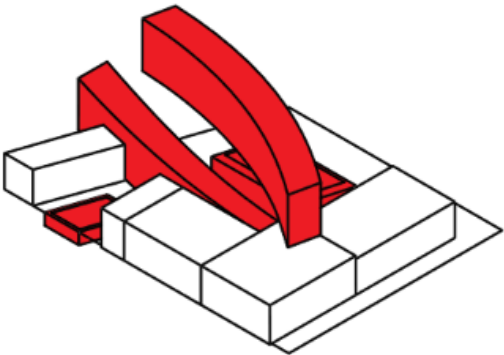


3. Add Guiding Masses and Pools

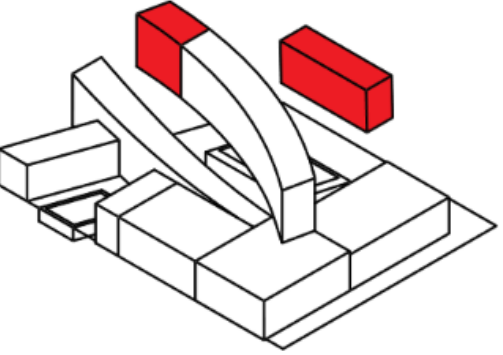


4. Expand Upward through Sauna Towards the Street

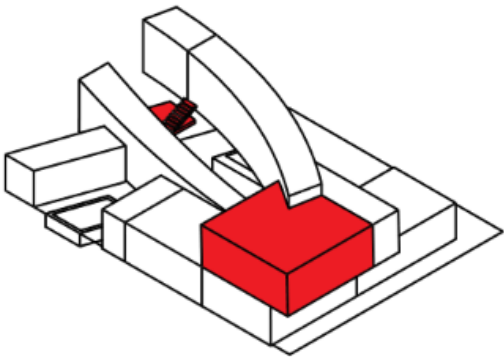

5. Double Height Space and Circulation between Two Floors

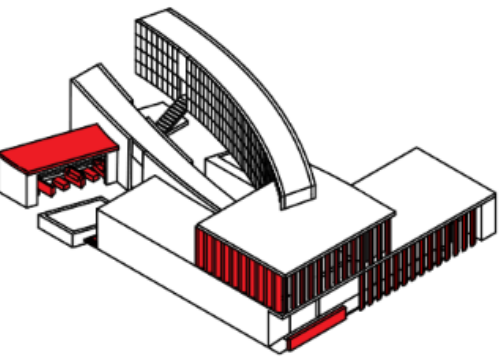

6. Daylighting Strategies in Louvers and Glazing

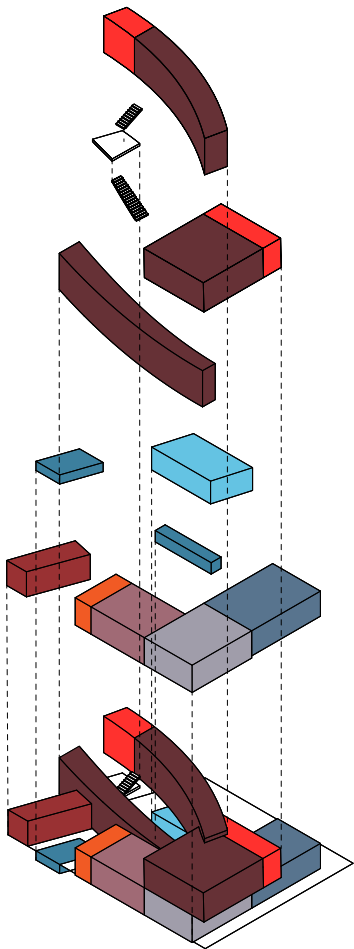

- large pool
- small pools
- 24 hour all-gender restroom
- sauna
- indoor lounge
- public / leisure space
- changing room / showers
- lobby
- site boundary
- single stall restroom

